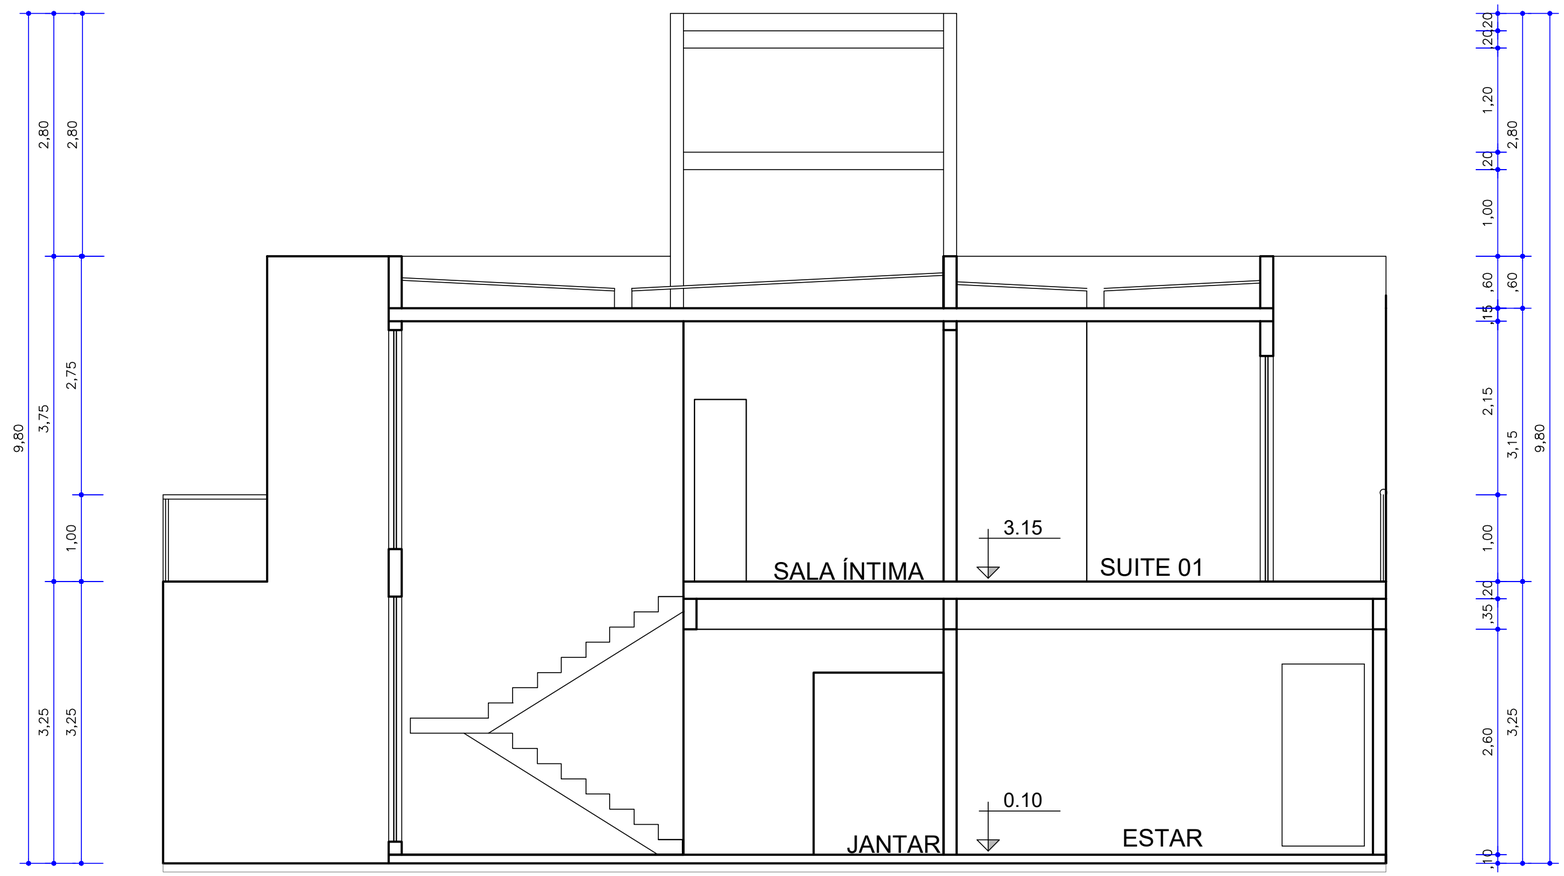


03 CORTE A

ESCALA: 1/50

UNIVERSIDADE SENAI CIMATEC

ESTUDO PREIMINAR

AV1 REPRESENTAÇÃO DIGITAL

Disciplina: REPRESENTAÇÃO DIGITAL DA CONSTRUÇÃO
Docente(s): Fernando Ferraz Ribeiro

Ano/Semestre: 2026.2

Discente(s): Marcos Cardoso & Nicolas Andrade


Prancha: 03 | 03

Escala: 1:50

CORTE A

Emissão: SET 2026

Revisão: 01 Data: 27/09/2026

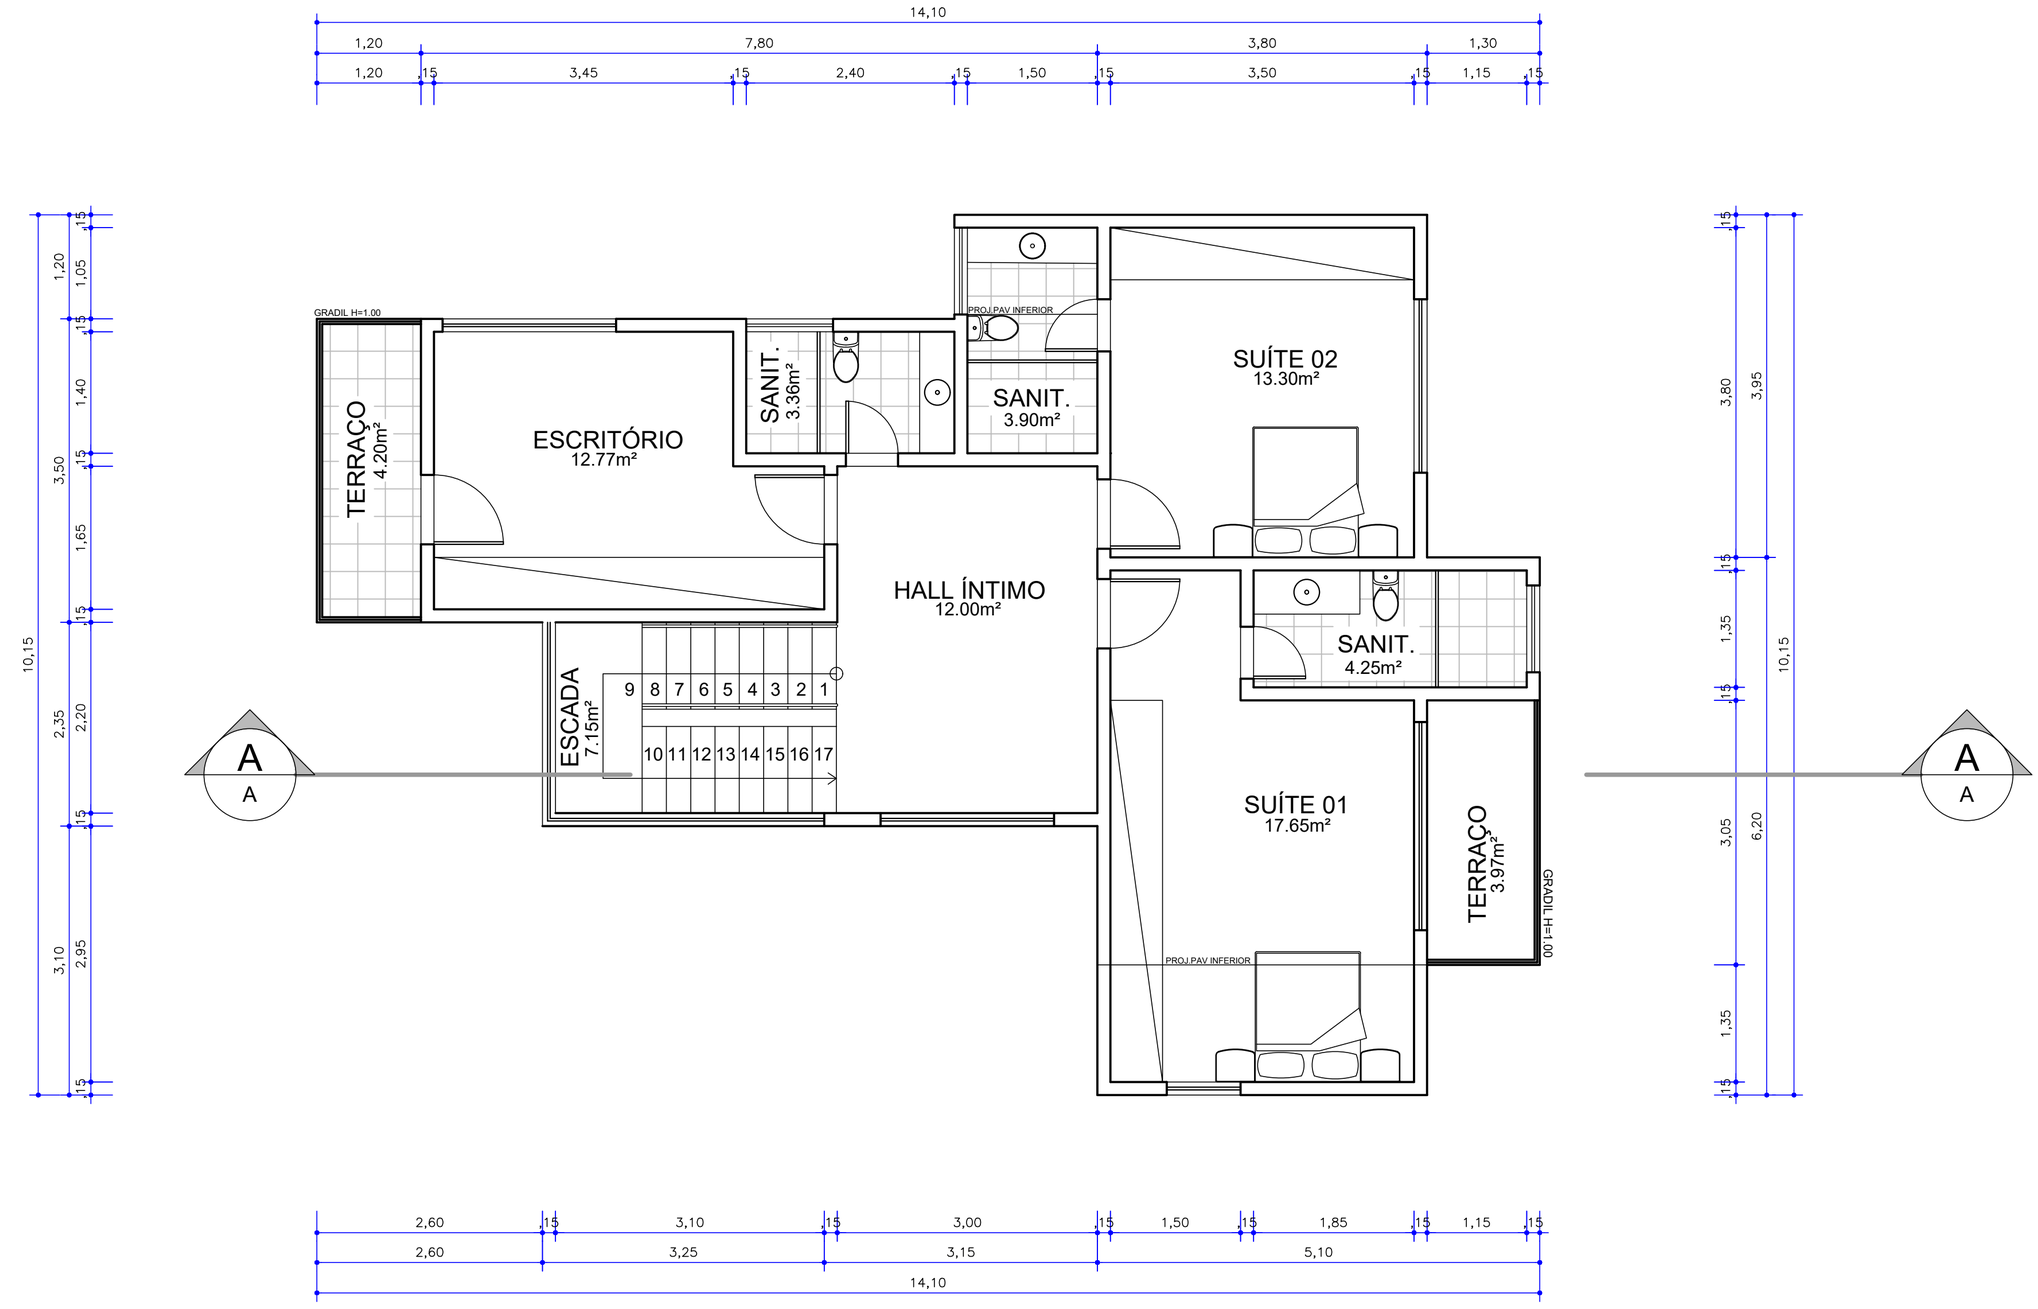

02 PLANTA PAV. SUPERIOR

ESCALA: 1/50

-
SUL

UNIVERSIDADE SENAI CIMATEC

ESTUDO PREIMINAR

AV1 REPRESENTAÇÃO DIGITAL


Disciplina: REPRESENTAÇÃO DIGITAL DA CONSTRUÇÃO
Docente(s): Fernando Ferraz Ribeiro
Ano/Semestre: 2026.2

Discente(s): Marcos Cardoso & Nicolas Andrade

Prancha: 02 | 03
Escala: 1:50
Emissão: SET 2026
Revisão: 01 Data: 27/09/2026

PLANTA PAV.SUPERIOR

QUADRO DE ESQUADRIAS		
COD.	QUANT.	DIMENSÕES
J1	5	2.00 x 1.20 h=1.00
J2	2	(2.35+3.10) x 2.70 h=0.20
J3	4	1.00 x 1.00 h=1.80
J4	1	2.00 x 1.10 h=1.20
J5	2	0.85 x 1.90 h=0.20
J6	2	0.95 x 1.90 h=0.20
P1	1	1.00 x 2.10
P2	7	0.8 x 2.10
P3	2	2.40 x 2.60
P4	3	0.60 x 2.10

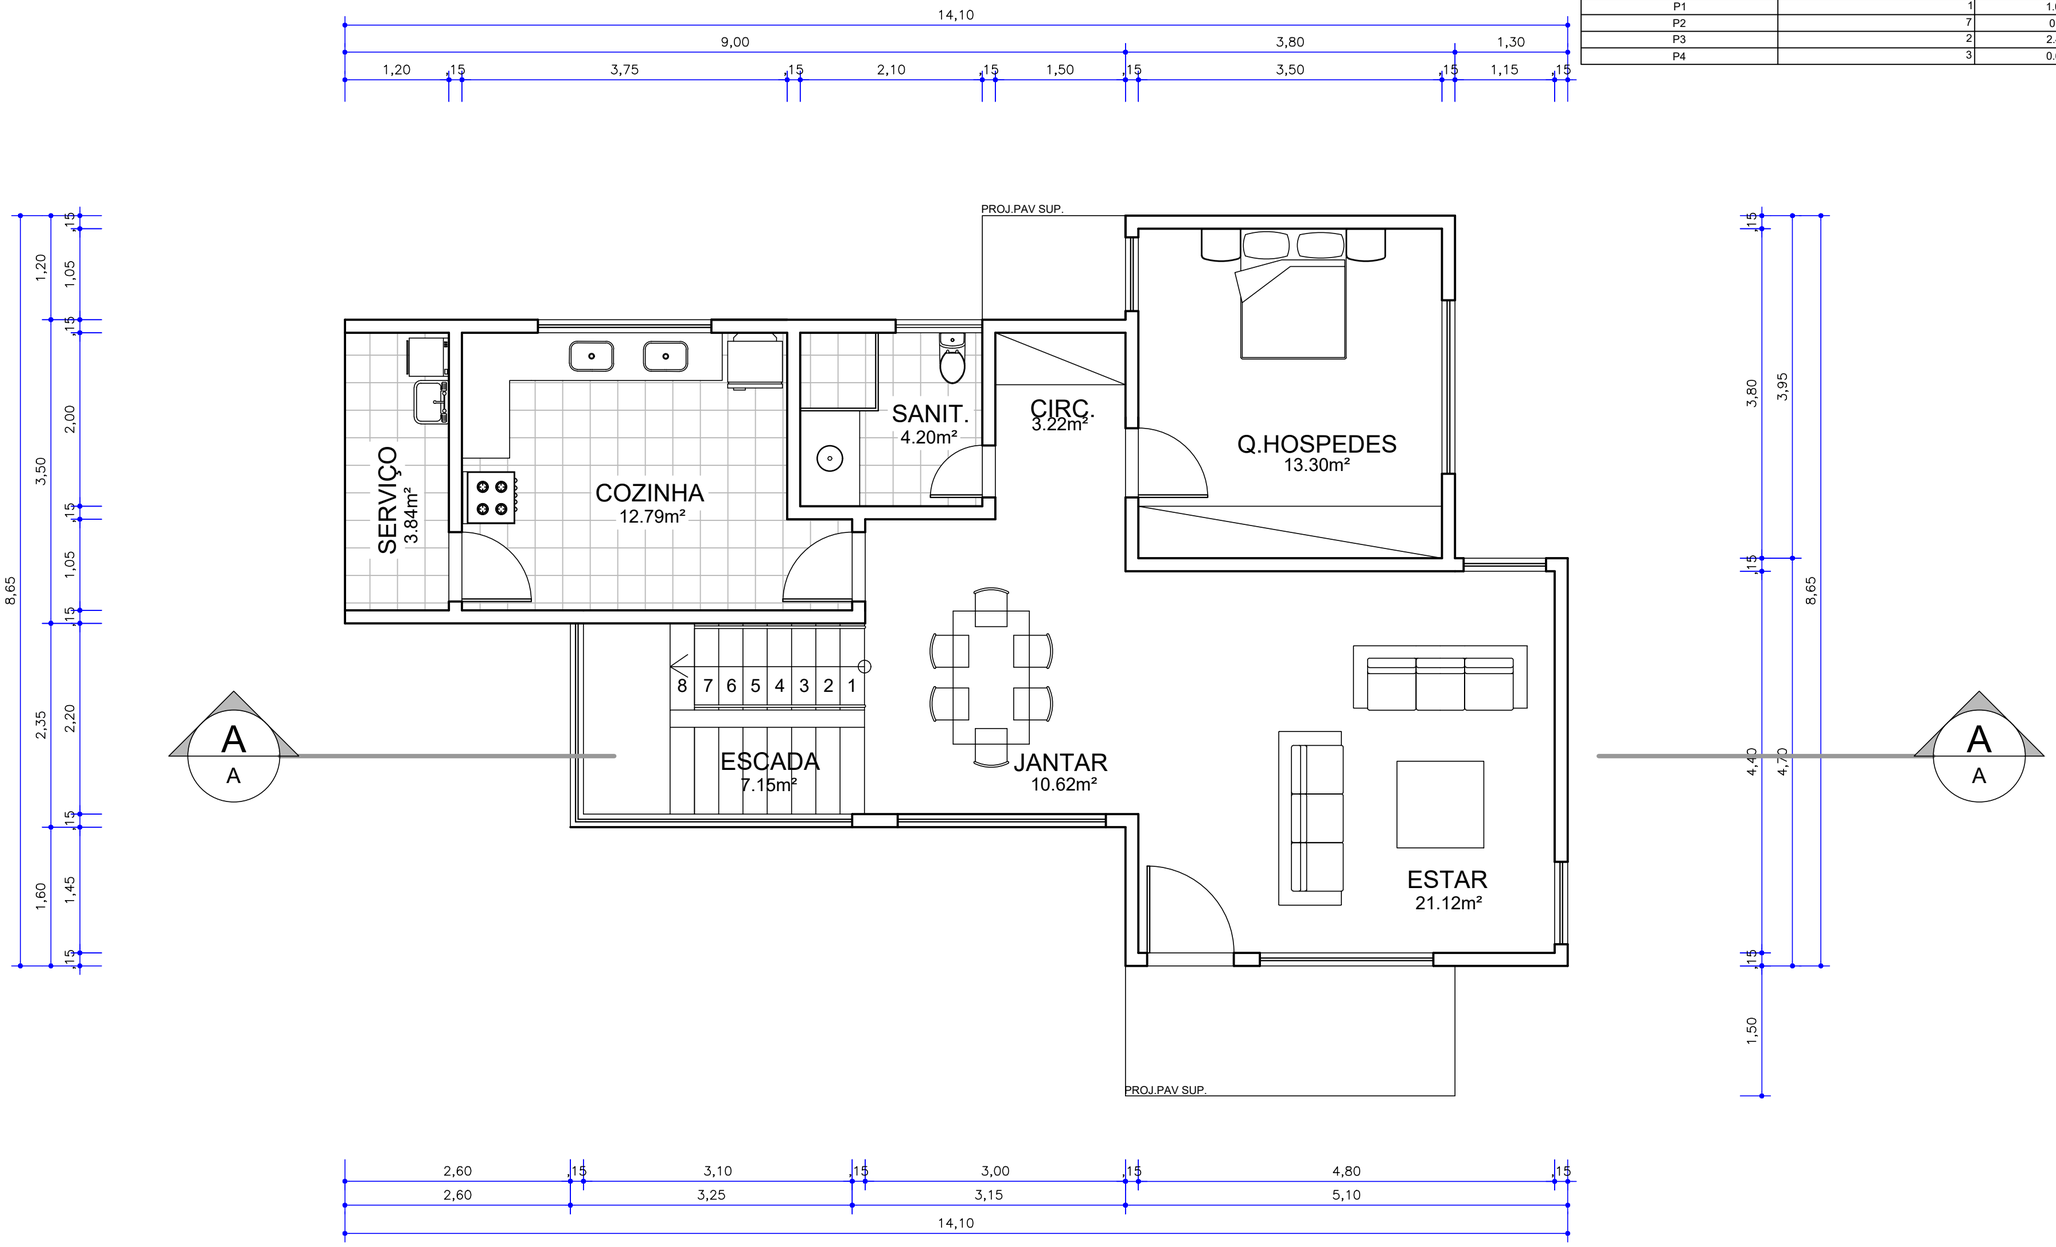

01 PLANTA TÉRREO

ESCALA: 1/50

SUL

UNIVERSIDADE SENAI CIMATEC

ESTUDO PREIMINAR

AV1 REPRESENTAÇÃO DIGITAL

Disciplina: REPRESENTAÇÃO DIGITAL DA CONSTRUÇÃO
Docente(s): Fernando Ferraz Ribeiro
Discente(s): Marcos Cardoso & Nicolas Andrade

Ano/Semestre: 2026.2

Prancha: 01 | 03

Escala: 1:50

Emissão: SET 2026

Revisão: 01 Data: 27/09/2026

PLANTA TÉRREO